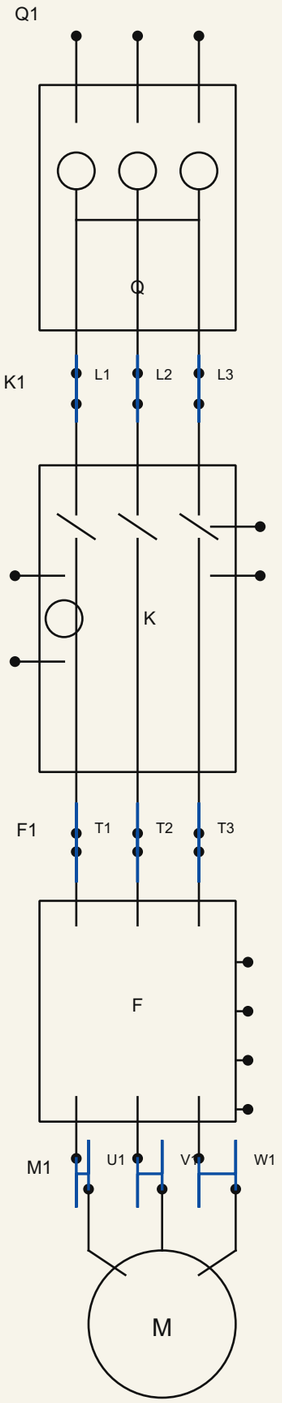

LOGO	COMPANY Acme Process Controls 12 Industrial Way PanelCAD 0.1.0	PROJECT DOL Motor Starter		REV	DATE	DESCRIPTION	DRAWN	CHK	APP
		TITLE Power		A	2026-08-19	Initial issue	PanelCAD		
		DESCRIPTION Motor power circuit							
		DWG No. E-001	STANDARD IEC	SHEET 1 / 3		SIZE A3 LAND		SCALE NTS	
		CUSTOMER Riverside Pump Station	LOCATION MCC-1 / Pump 1	DRAWN PanelCAD		CHECKED		APPROVED	

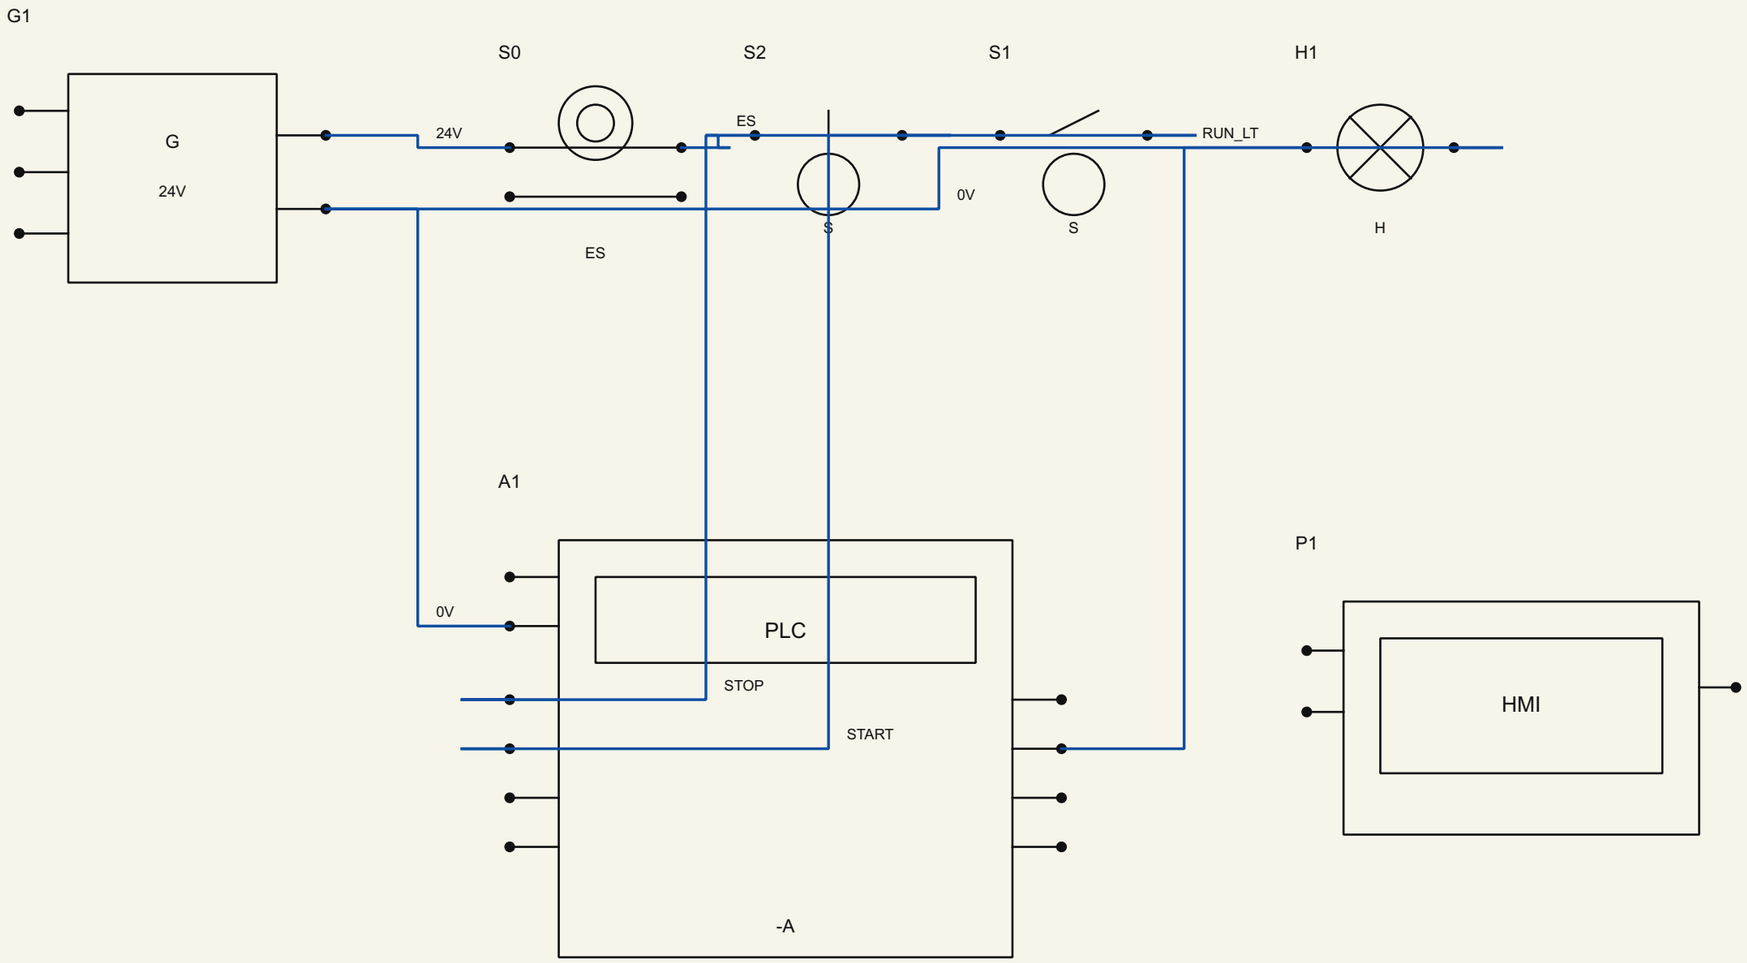

LOGO	COMPANY Acme Process Controls 12 Industrial Way PanelCAD 0.1.0	PROJECT DOL Motor Starter		REV	DATE	DESCRIPTION	DRAWN	CHK	APP
		TITLE Control		A	2026-08-19	Initial issue	PanelCAD		
		DESCRIPTION 24 VDC control, PLC and operator devices							
		DWG No. E-001	STANDARD IEC	SHEET 2 / 3		SIZE A3 LAND		SCALE NTS	
		CUSTOMER Riverside Pump Station	LOCATION MCC-1 / Pump 1	DRAWN PanelCAD		CHECKED		APPROVED	

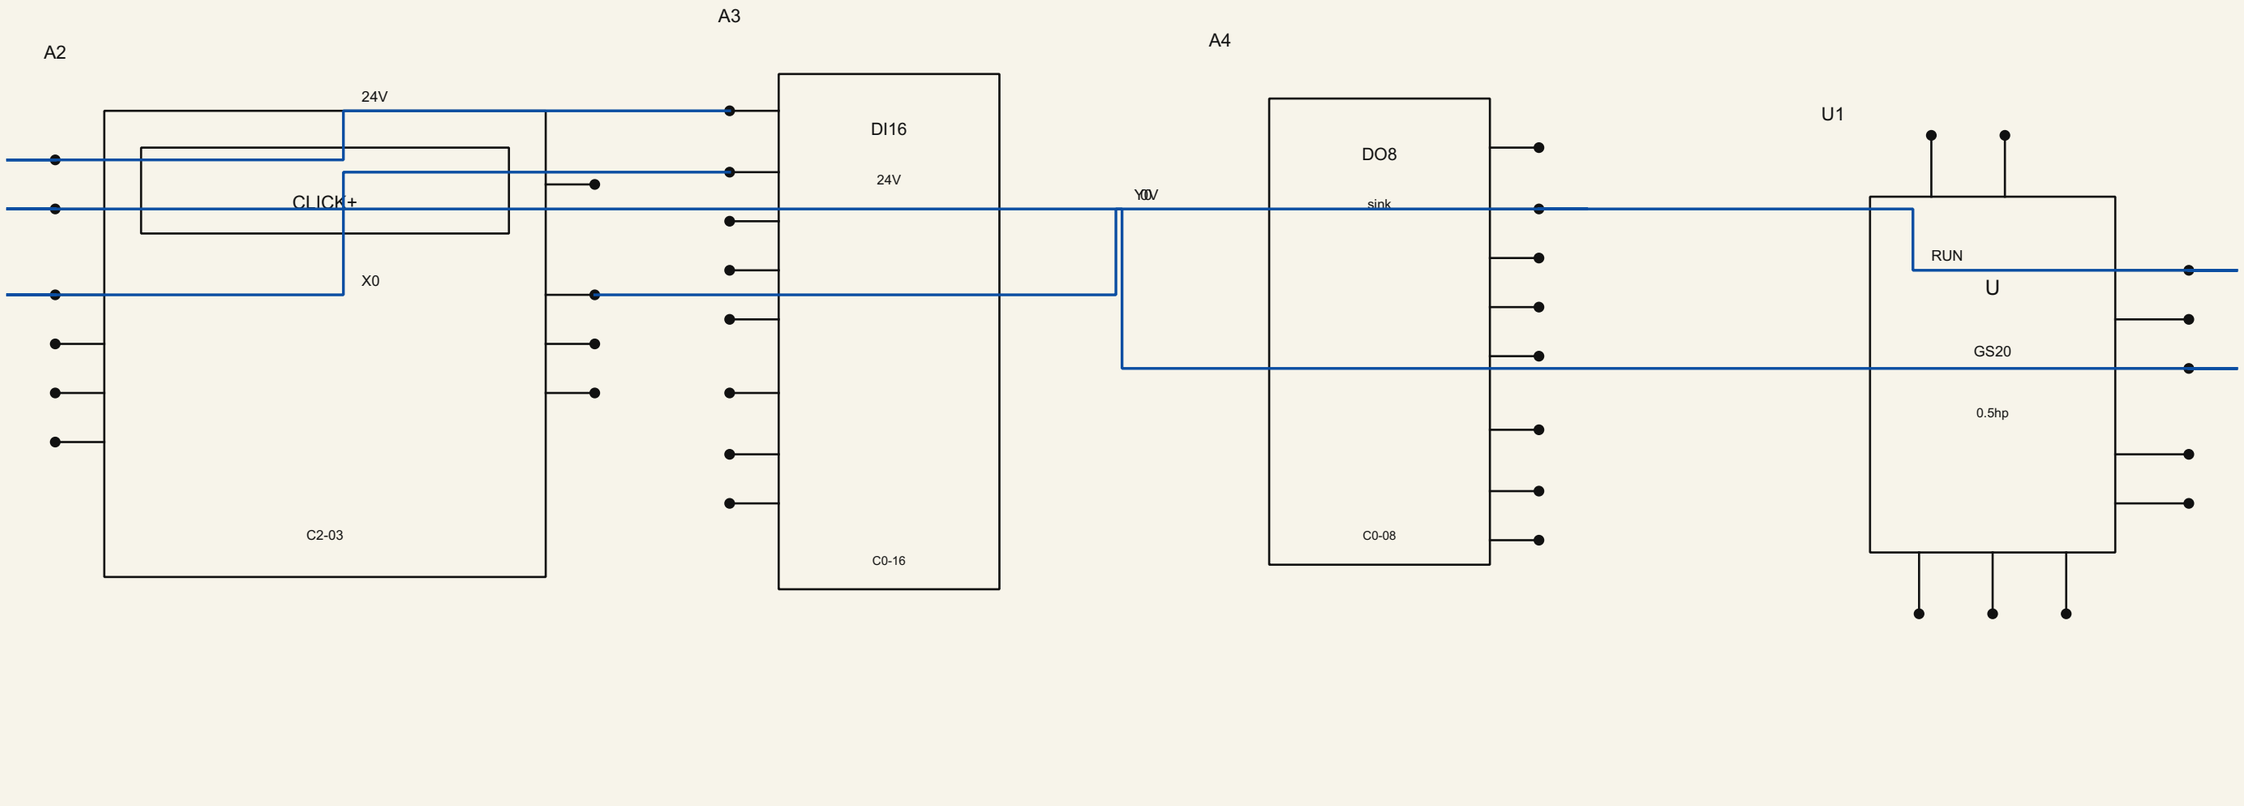

LOGO	COMPANY Acme Process Controls 12 Industrial Way PanelCAD 0.1.0	PROJECT DOL Motor Starter		REV	DATE	DESCRIPTION	DRAWN	CHK	APP
		TITLE PLC I/O and VFD		A	2026-08-19	Initial issue	PanelCAD		
		DESCRIPTION CLICK stackable I/O and DURApulse GS20							
		DWG No. E-001	STANDARD IEC	SHEET 3 / 3		SIZE A3 LAND		SCALE NTS	
		CUSTOMER Riverside Pump Station	LOCATION MCC-1 / Pump 1	DRAWN PanelCAD		CHECKED		APPROVED	